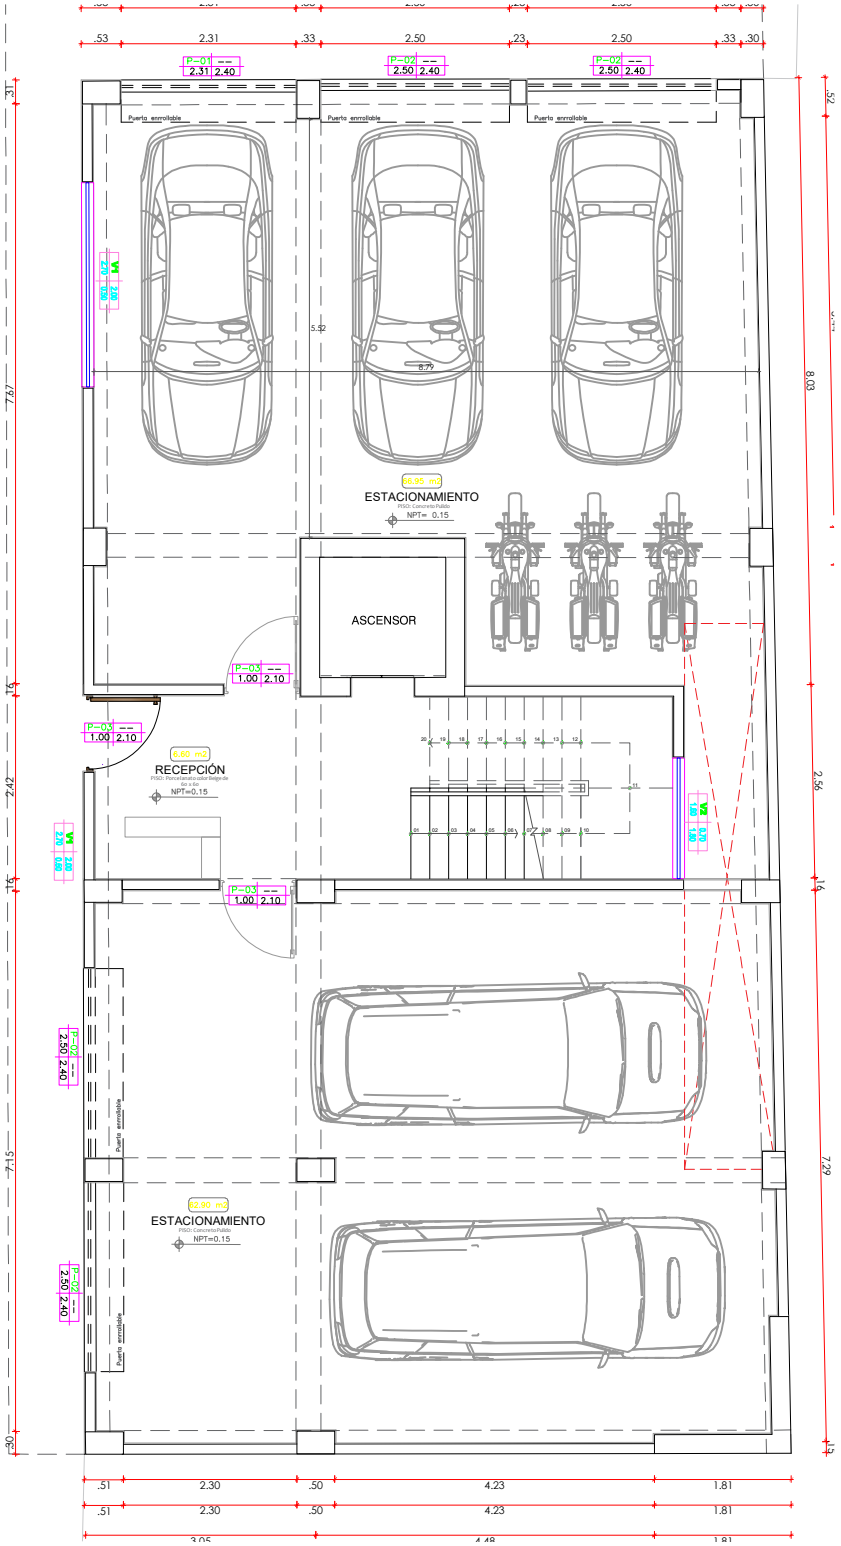
ESTACIONAMIENTO
PISO: Concreto Pulido
NPT= 0.15
ASCENSOR
RECEPCIÓN
PISO: Porcelanato Rectificado
NPT=0.15
ESTACIONAMIENTO
PISO: Concreto Pulido
NPT=0.15
Puerta enrollable
P-01 2.31 2.40
P-02 2.50 2.40
P-03 1.00 2.10
.53
2.31
.33
2.50
.23
2.50
.33
.30
8.03
2.56
7.29
.51
2.30
.50
4.23
1.81