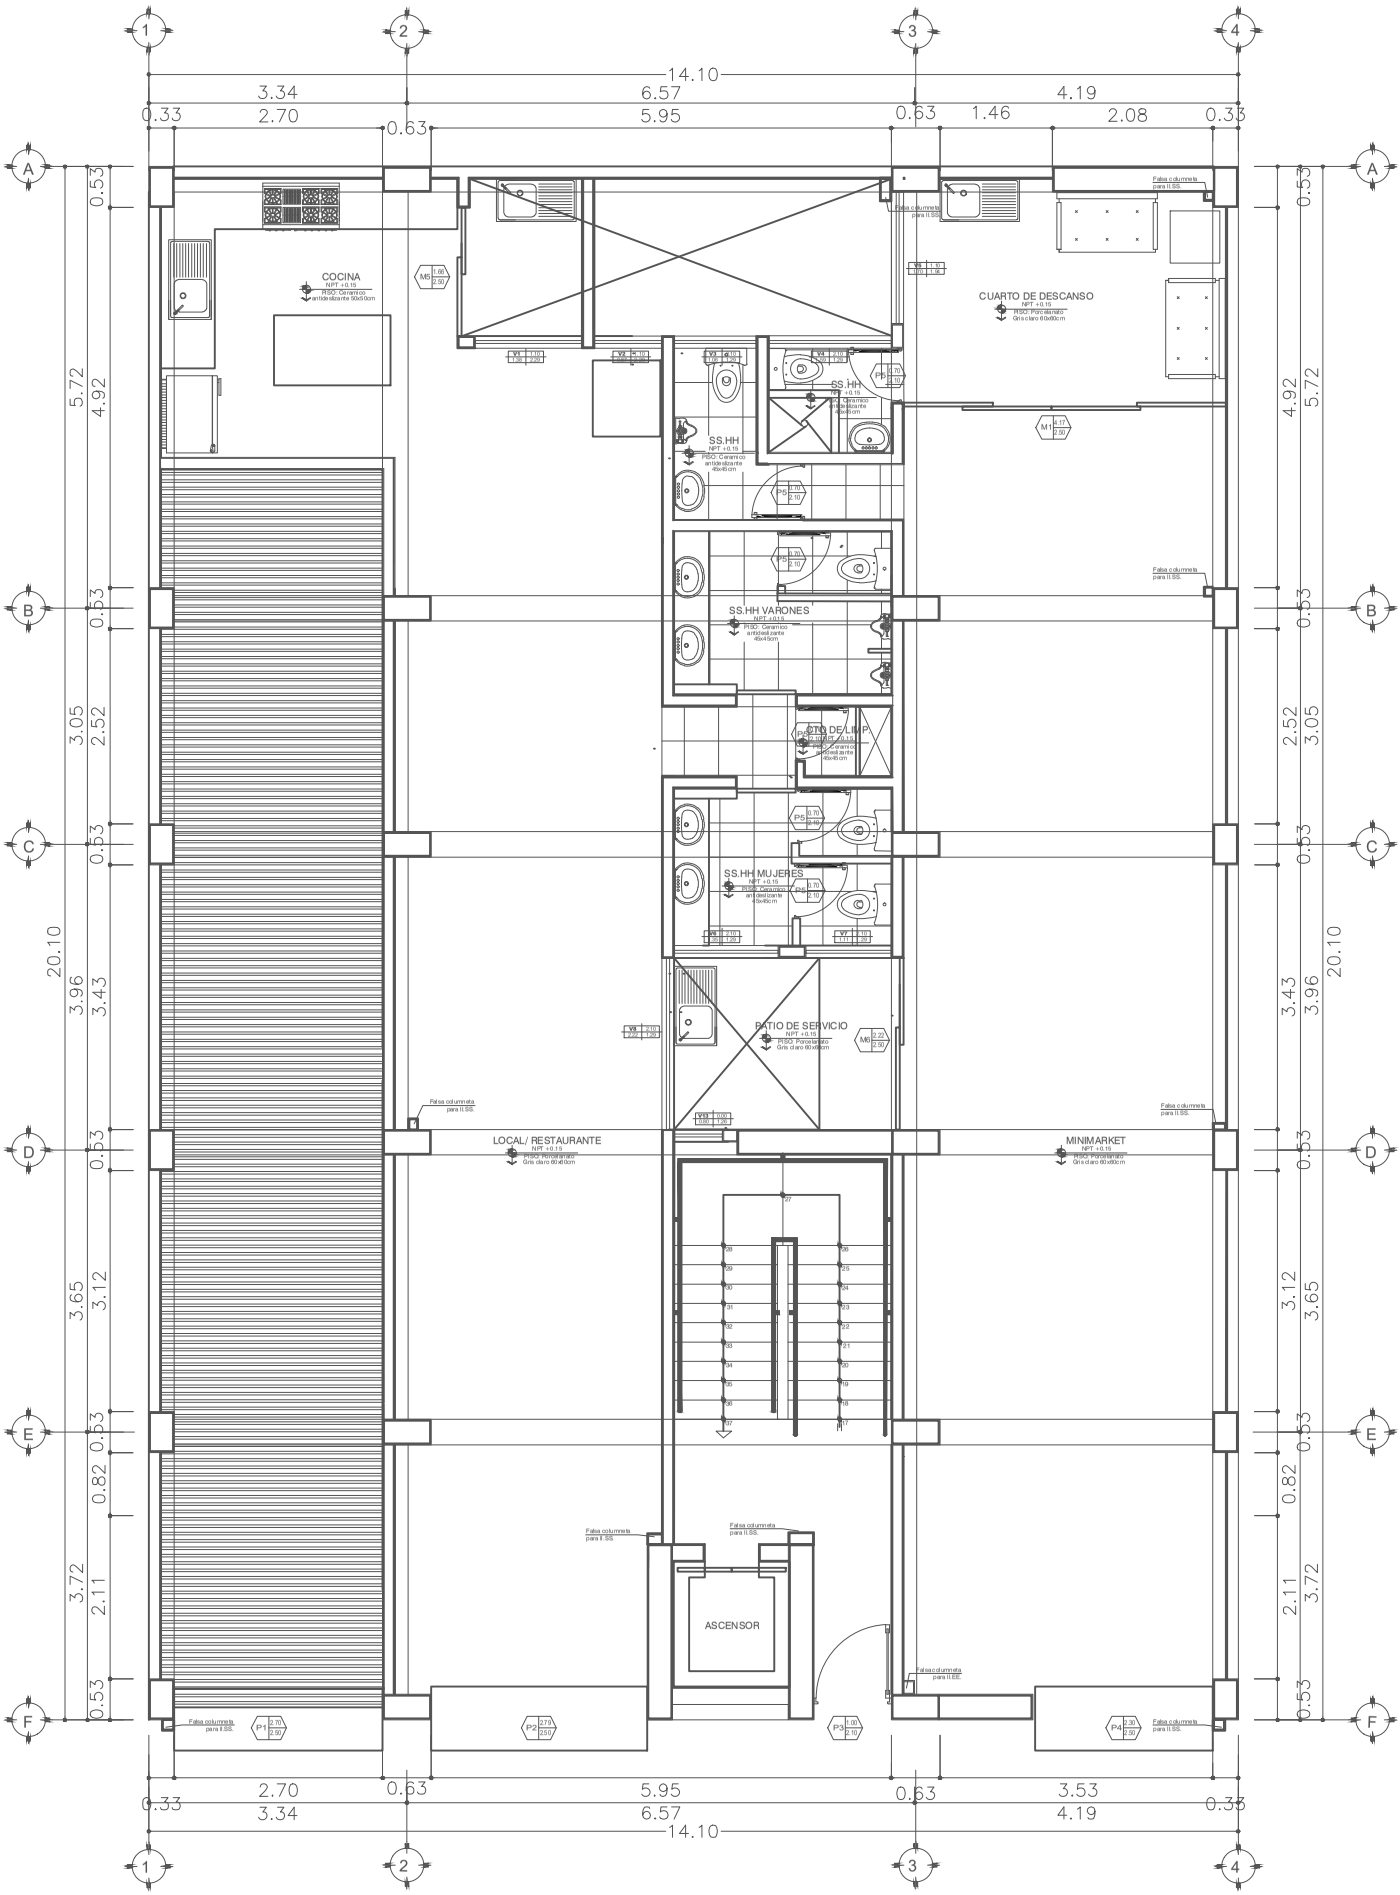
COCINA
NPT +0.15
PISO: Ceramico antideslizante 50x50cm
CUARTO DE DESCANSO
NPT +0.15
PISO: Porcelanato Gris claro 60x60cm
SS.HH
NPT +0.15
PISO: Ceramico antideslizante 45x45cm
SS.HH VARONES
NPT +0.15
PISO: Ceramico antideslizante 45x45cm
PATIO DE LIMP.
NPT +0.15
PISO: Ceramico antideslizante 45x45cm
SS.HH MUJERES
NPT +0.15
PISO: Ceramico antideslizante 45x45cm
PATIO DE SERVICIO
NPT +0.15
PISO: Porcelanato Gris claro 60x60cm
LOCAL/ RESTAURANTE
NPT +0.15
PISO: Porcelanato Gris claro 60x60cm
MINIMARKET
NPT +0.15
PISO: Porcelanato Gris claro 60x60cm
ASCENSOR
Falsa columneta para II.SS.
Falsa columneta para II.EE.
14.10
20.10